ARIF RAIHAN

ARCHITECTURE

SELECTED WORK / 2026

Forms of collective life

A composition of selected project forms

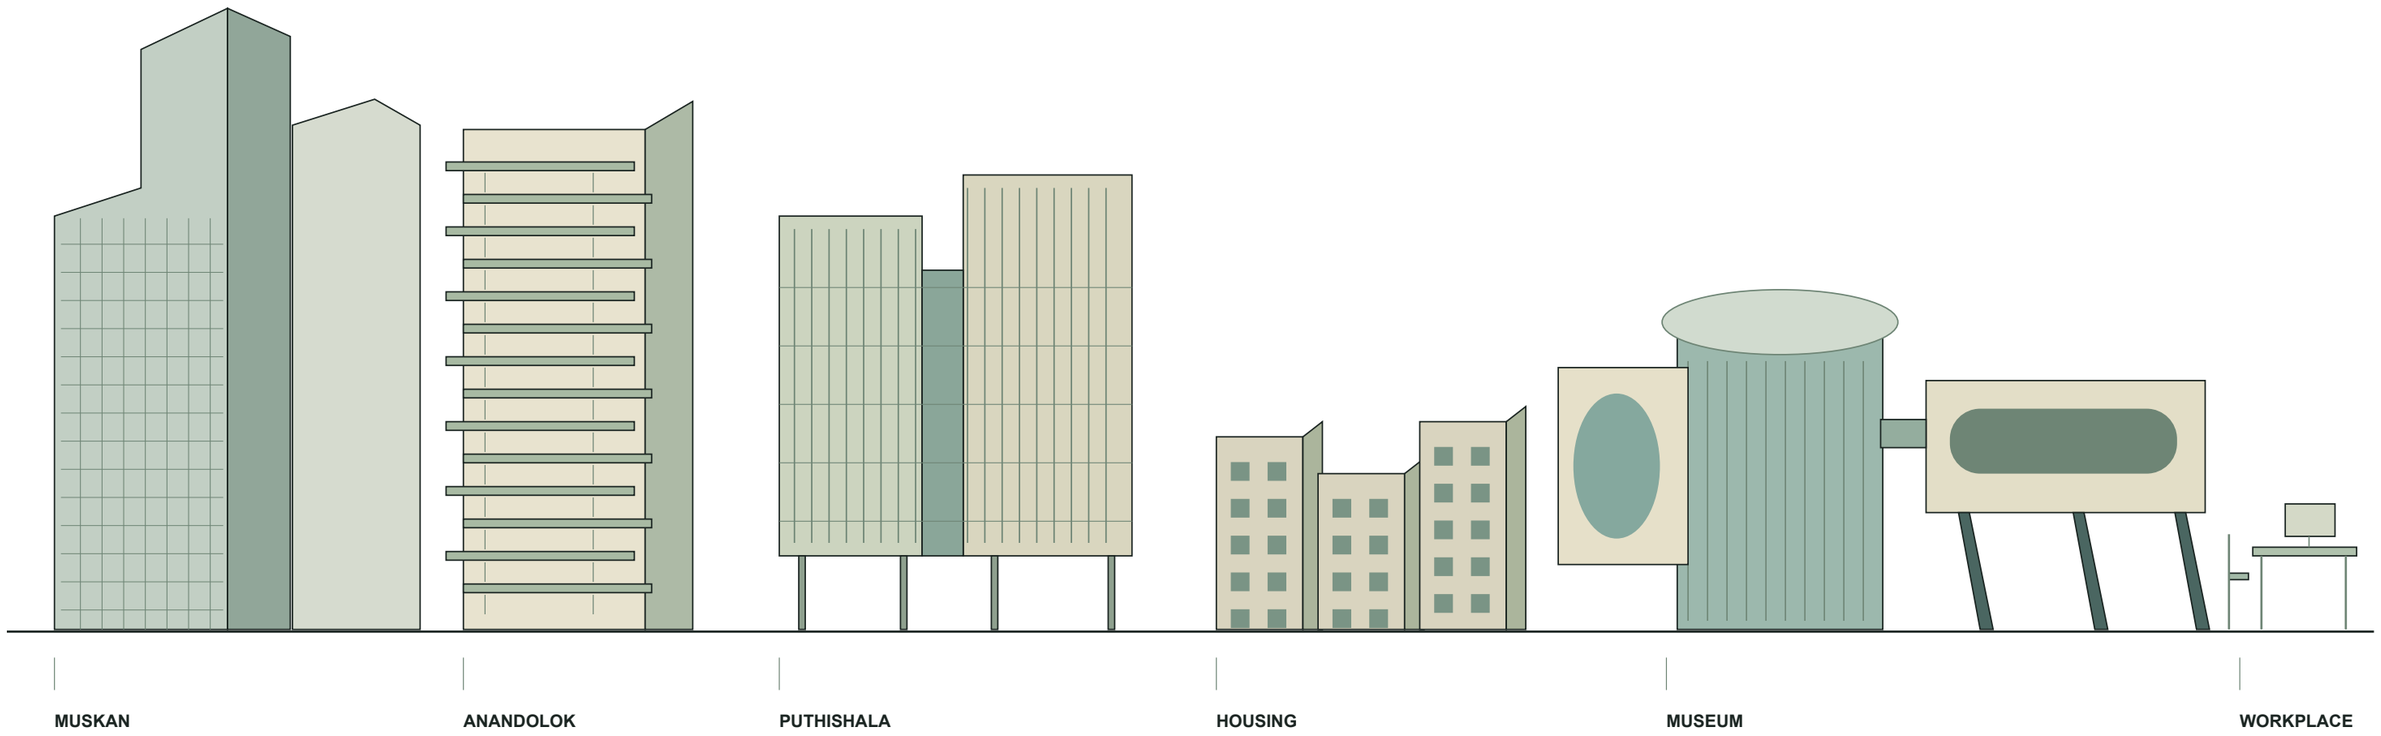

Design / Detail / Place

Professional + academic projects

FORM STUDIES / NOT TO SCALE

Profile & selected work

Arif Raihan / Dublin, Ireland

Architecture, from design to detail and delivery.

Lobby, furniture and signage design

Drawing and detail development

Consultant and site coordination

Materials and workmanship review

MBA, Project Management / DBS / 2026

B.Arch / BRAC University / 2021

AutoCAD / SketchUp / Adobe Creative Suite

V-Ray / Twinmotion / Lumion / MS Project

Muskan Tower 003

Anandolok 008

Shanta Forum HQ 013

Puthishala 017

Bhashantek Housing 020

Sylhet Divisional Museum 024

Muskan Tower

Commercial / Dhaka

Suvastu / 2024-2025

Reception & lobby

All site signage

Details & finishing coordination

Suvastu / Design: Arif Raihan / Photography: City Syntax

Arrival & identity

Muskan Tower / Reception, lobby and site signage

01 / LOBBY INTERIOR

02 / RECEPTION & DIRECTORY

Material selection / drawing to site

Muskan Tower / Palette, joint set-out and cost-control intent

01 / SOURCE DRAWING

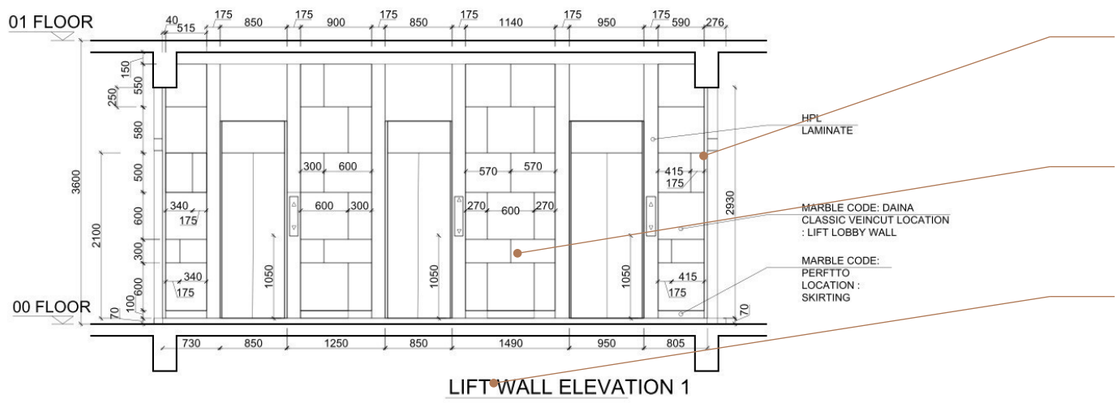

D-024 / Lift-wall elevation / 02 April 2022

02 / MATERIAL COORDINATION

A

HPL accents

Locate laminate within the material hierarchy.

B

Marble fields + skirting

Daina Classic wall fields / Perfito skirting in the source key.

C

Set-out before procurement

Check joint positions, cut sizes and interfaces together.

03 / COMPLETED LOBBY

04 / BASEMENT COLUMN GUARD - FIXING SECTION

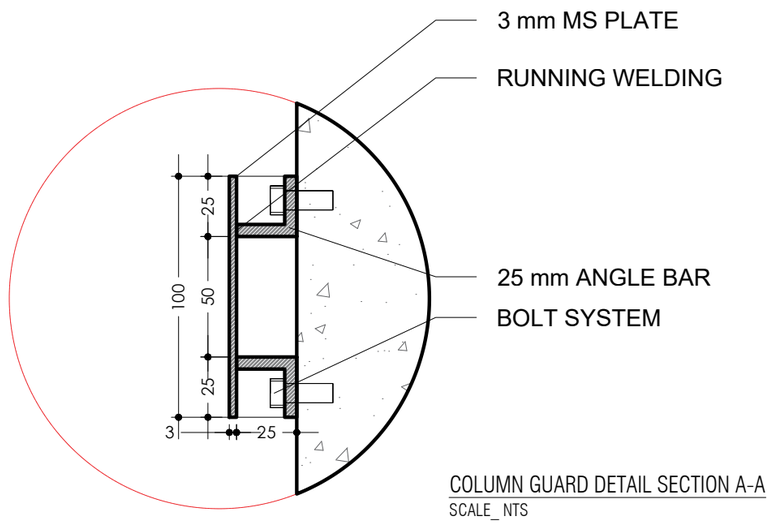

Original CAD / Guard assembly beside ramps and parking

Suvastu / Source D-024: Volume Zero Architects / Material selection: Arif Raihan / Photo: City Syntax

Railing & roof junctions

Muskan Tower / Original CAD extracts / NTS

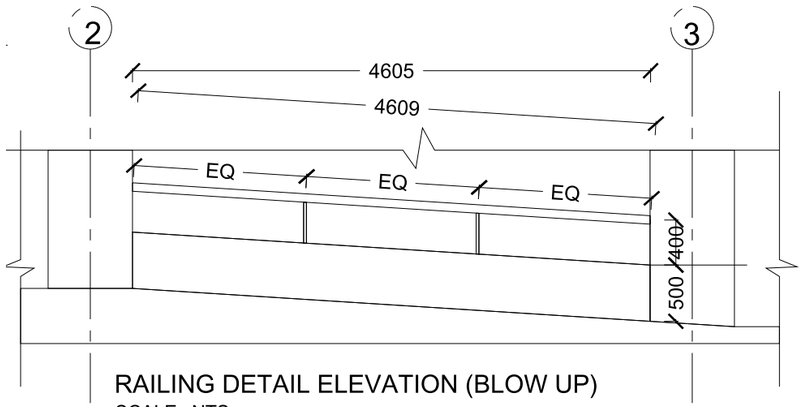

RAILING DETAIL ELEVATION (BLOW UP)
SCALE_ NTS

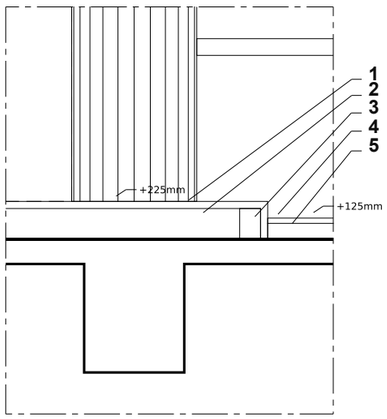

Blowup detail -2

SOURCE MATERIAL KEY

01 Semi-Outdoor Floor Finish

02 Foam Concrete

03 Brick

04 Outdoor Floor Finish

05 Foam Concrete

03 / ROOF JUNCTION / SOURCE DETAIL 2

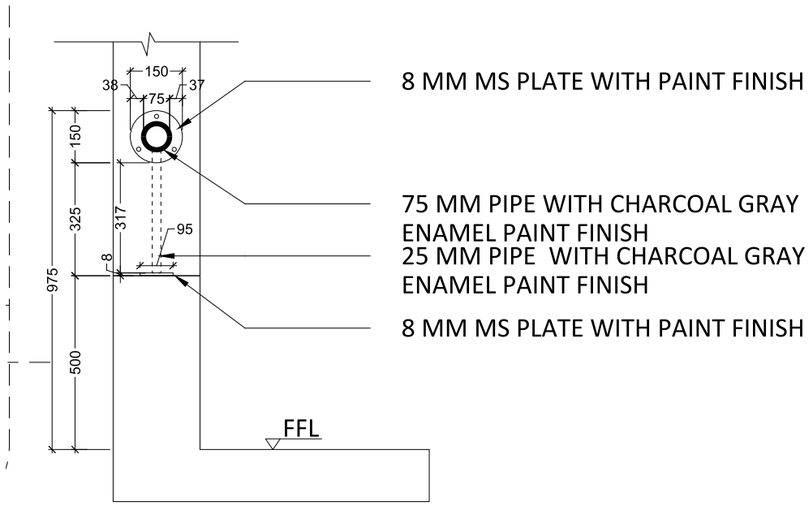

RAILING DETAIL SECTION A-A
SCALE_ NTS

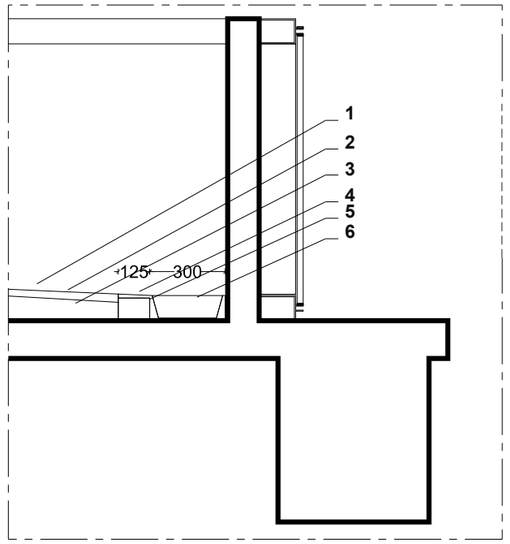

Blowup detail -1

SOURCE MATERIAL KEY

01 Slope +125mm to +100mm

02 Outdoor Floor Finish

03 Foam Concrete

04 Net Cement Finish

05 Brick

06 Gravel for rain water drainage

Basement column protection

Muskan Tower / Ramp-side and parking columns / Two source guard assemblies / CAD dimensions in mm / NTS

01 / CONTINUOUS GUARD

PLAN

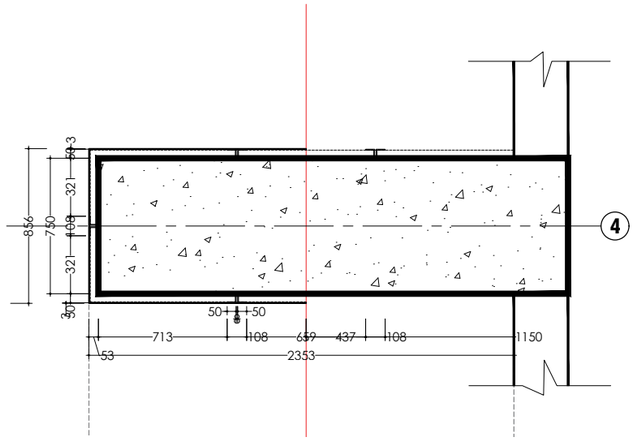

ELEVATION / FRAME & TERMINATIONS

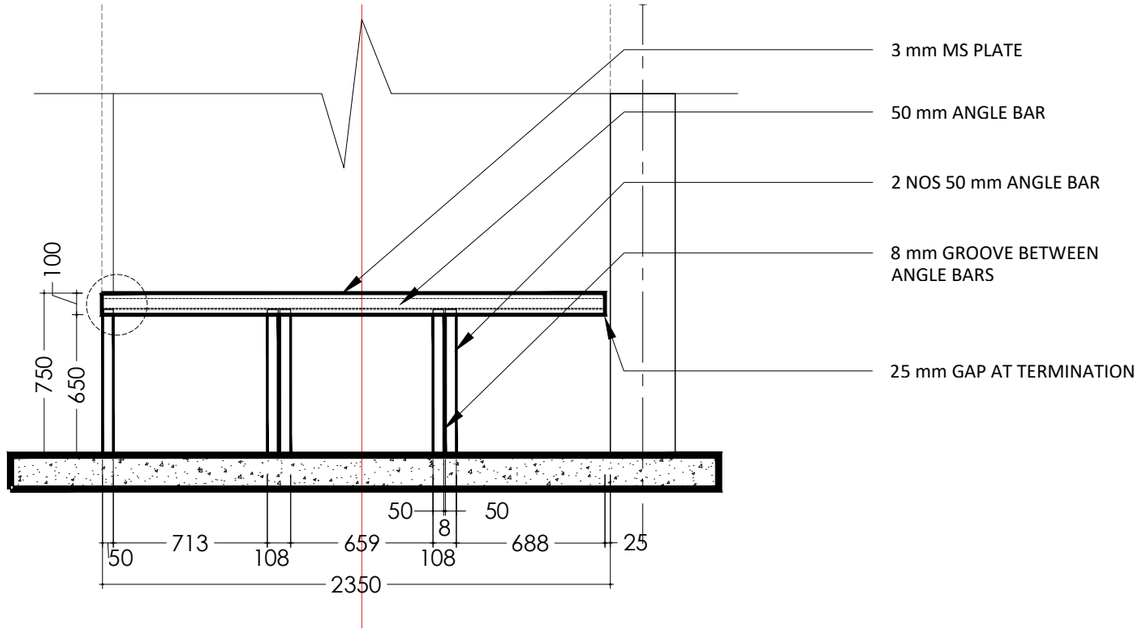

3 mm plate / 50 mm angle bars / Welded and bolted supports

02 / LOCAL GUARD

PLAN

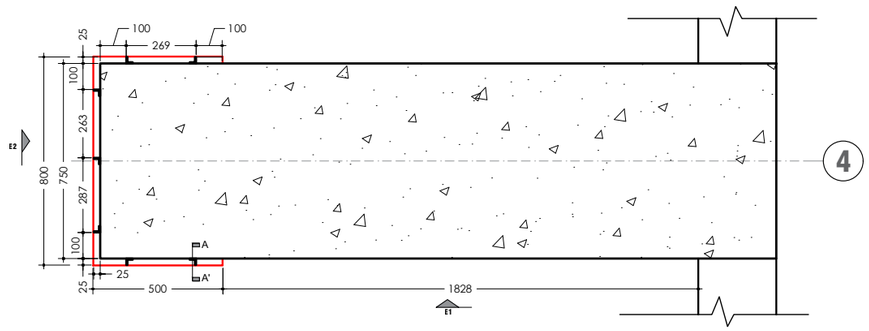

COLUMN GUARD PLAN
SCALE _ NTS

ELEVATION / LOCAL PROTECTION

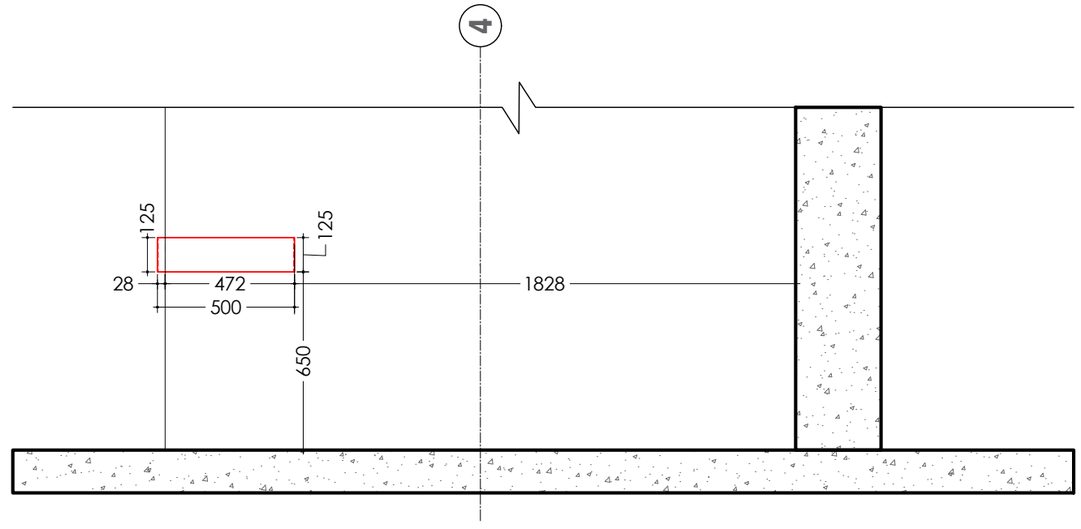

COLUMN GUARD ELEVATION 1
SCALE _ NTS

3 mm plate / 25 mm angle / Local fixing and end protection

Suvastu / Source CAD sheets: Volume Zero Architects / Detail development and site coordination: Arif Raihan

Anandolok

Residential / Dhaka

15 storeys / 24 apartments

Suvastu / 2022-2024

Reception & entry lobby

All site signage

Details, coordination & inspections

Suvastu / Design: Arif Raihan / Photography: City Syntax

Window & grille assembly

Anandolok / Original CAD / NTS

01 / WINDOW SECTION

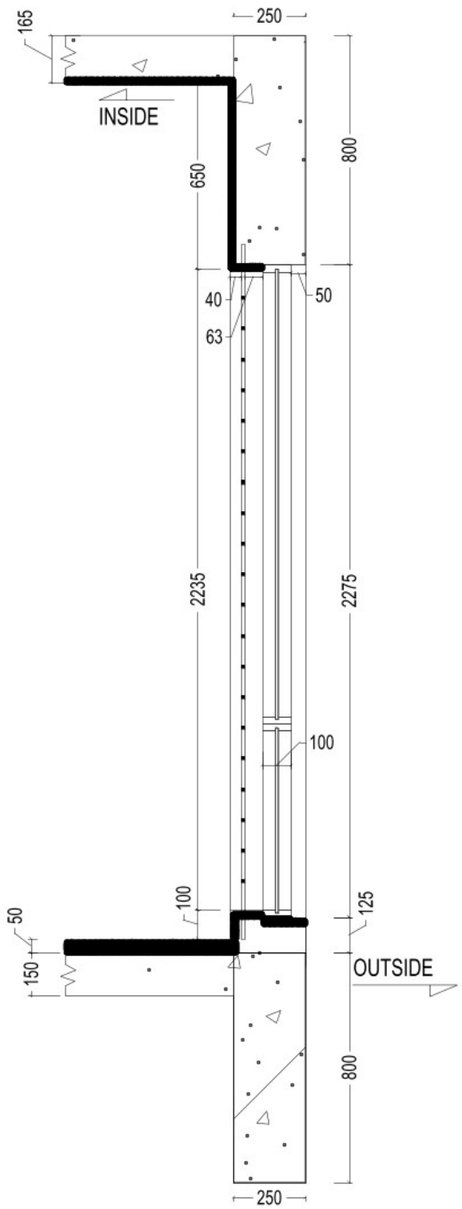

02 / PLAN

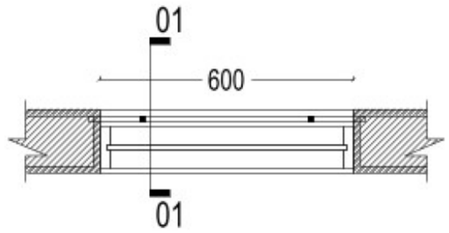

03 / GLASS ELEVATION

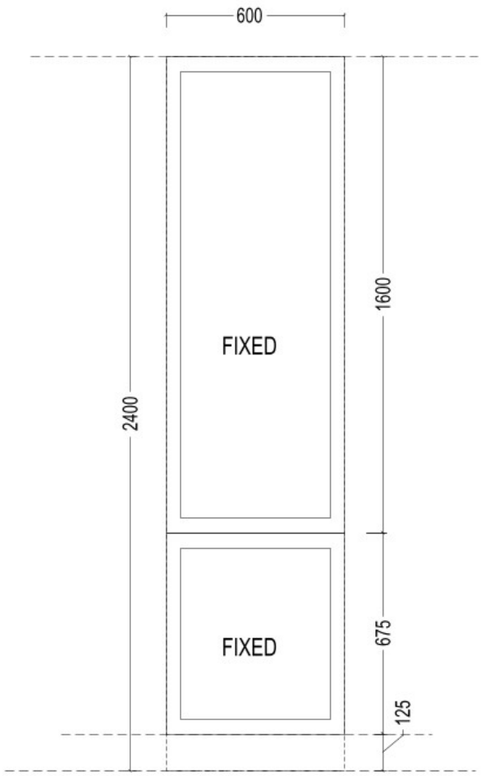

04 / GRILLE ELEVATION

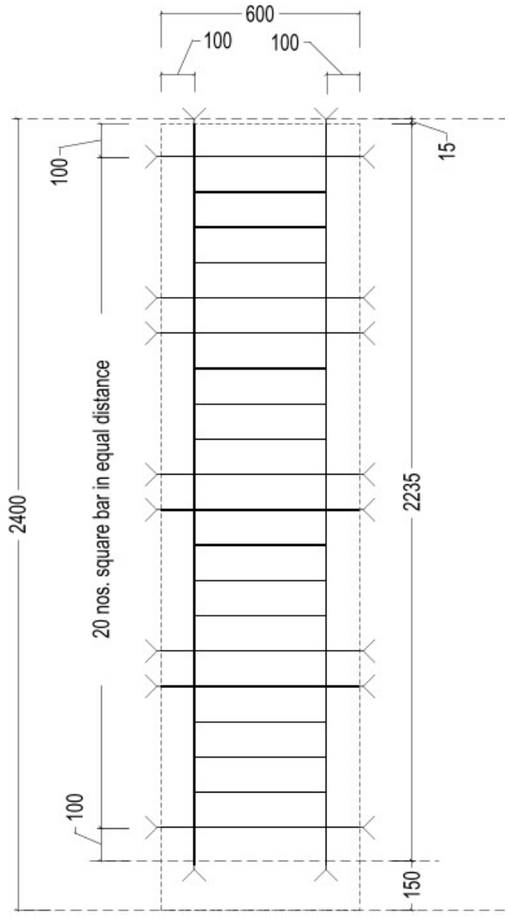

Arrival, stair & landscape

Anandolok / Completed work

01 / RECEPTION & ENTRY LOBBY

02 / STAIR, POOL & PLANTING

Precision in the stair railing

Anandolok / Angled rhombus panels / Built detail

STAIR SET-OUT & JOINERY

Millimetre set-out of the stair to coordinate the angled metal panels and their connections.

BUILT / PERFORATED METAL PANELS

Reception / original drawings & built

Muskan Tower / Plan, elevations and sections from the supplied reception-desk CAD / Dimensions in mm / NTS

01 / PLAN

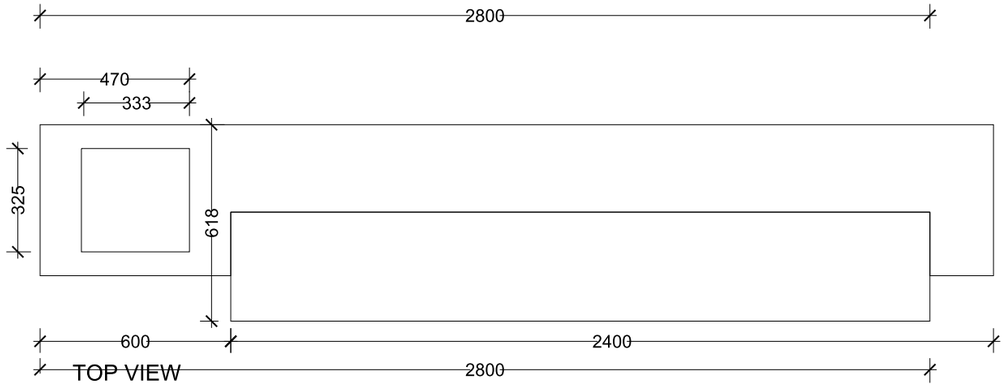

02 / FRONT ELEVATION

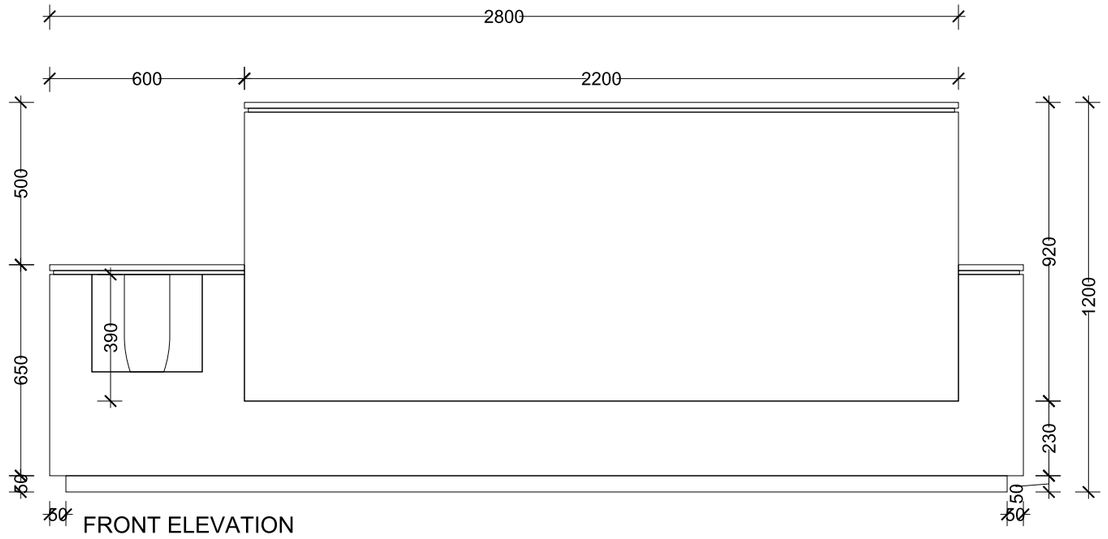

03 / SECTIONS A-A & B-B

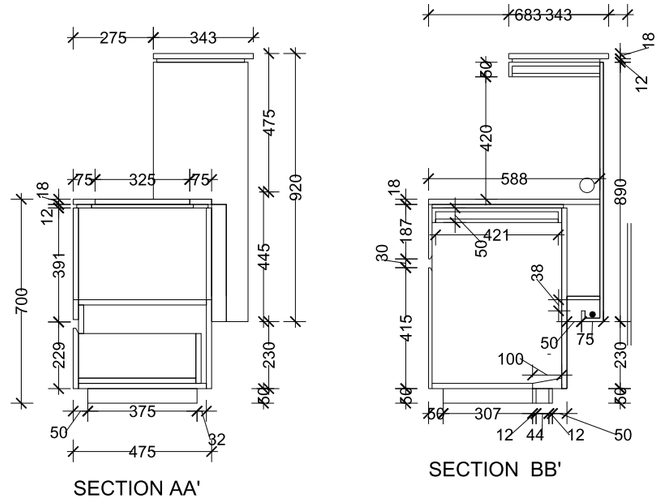

04 / COMPLETED DESK

Reception design: Arif Raihan / Original project CAD geometry and dimensions / Photography: City Syntax

Shanta Forum HQ

Workplace / Dhaka

Domus Architects / 2022

Three floors / approx. 60,000 sq ft

Spatial design assistance

Bespoke furniture & details

3D development

Site surveys & inspections

Arif Raihan / 2026

Workplace character

Shanta Forum HQ / Spatial design & visualization

01 / OPEN WORKPLACE

02 / MEETING SPACE

Boardroom table

Shanta Forum HQ / Furniture development study / Nominal dimensions in mm / NTS

01 / PLAN

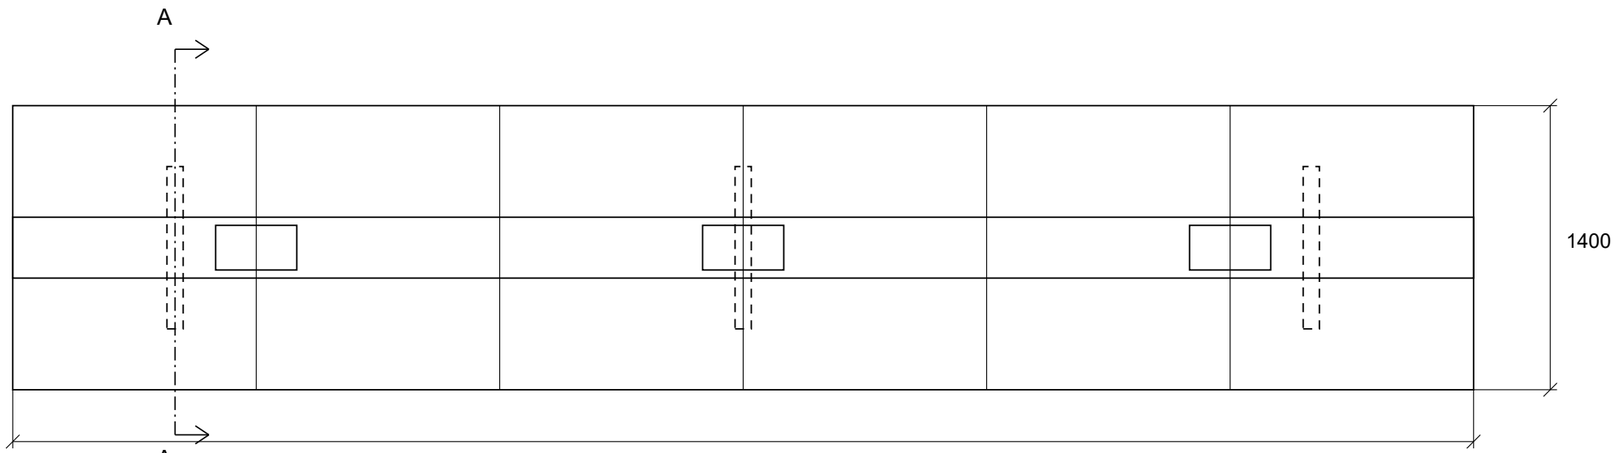

Six nominal modules at 1200 / dashed support frames below

02 / LONG ELEVATION

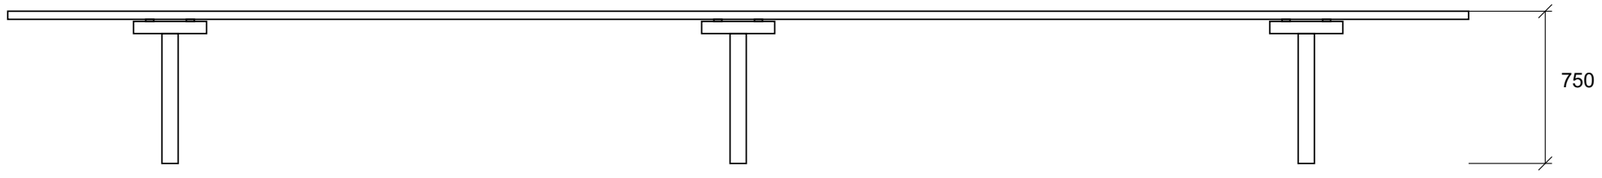

03 / SECTION A-A

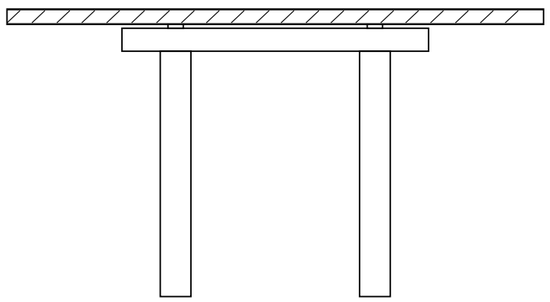

T01 / 40 top: 36 core + 2 facing each side

P01 / 10 pads | F01 / 60 rail, 640 leg zone

Support frame centres: 800 / 3600 / 6400.

S01 / 400 x 220 service openings in plan.

Nominal dimensions in mm / NTS.

Power & data access / Removable top panels / Independent support frames

Furniture / junction & construction

Shanta Forum HQ / Proposed development details / Nominal dimensions in mm / NTS

D05 / TOP FIXING & SUPPORT

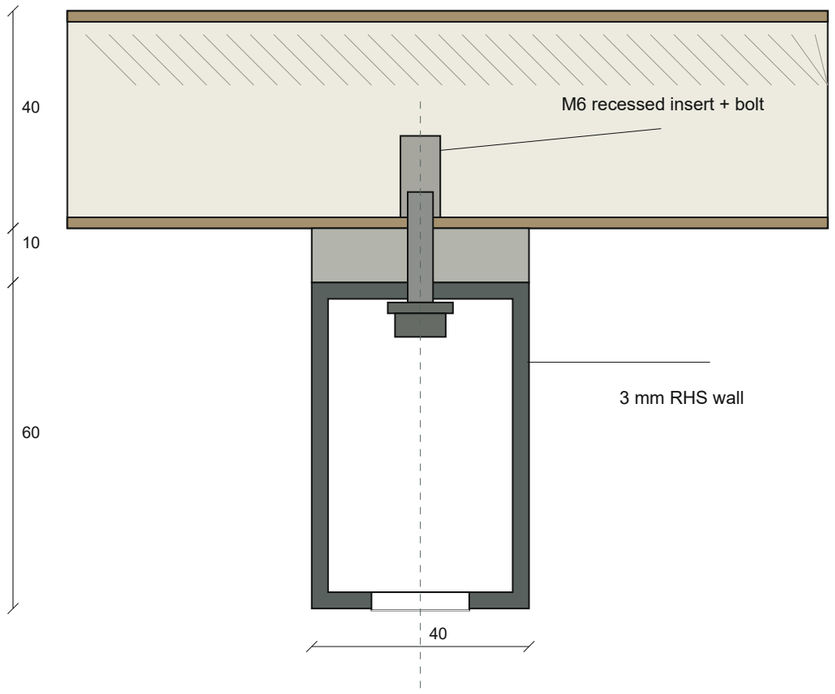

Tool access from below

Top: 2 finish + 36 core + 2 balancing face = 40 / 10 isolation pack / 40 x 60 x 3 RHS / Proposed build-up

D06 / LIFT-OUT SERVICE COVER

40 top / 10 isolation pack / 60 RHS

Cover lifts freely; tray and hangers remain fixed to the frame.

15 mm cover bearing each side / Confirm screw edge distances and loads.

D03 / PANEL JOINT

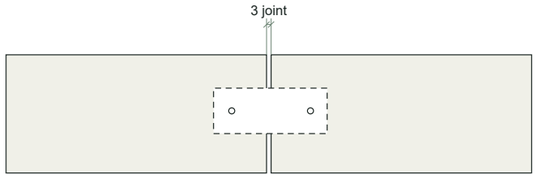

Panel joint with underside alignment plate

Dry-fit before machining; retain access from below.

D04 / LEVELLING FOOT

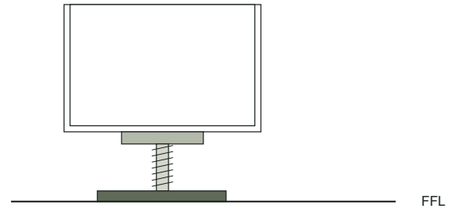

Threaded levelling foot / floor protection

Maintain tool access. Hardware and capacities by fabricator.

Puthishala

Edutainment Center / Shahbagh, Dhaka / Individual academic design

01 / LIBRARY ABOVE PUBLIC GROUND

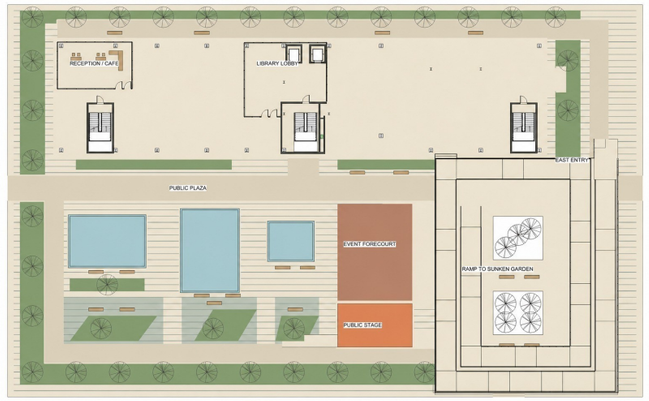

02 / GROUND PLAN / NTS

Read above.
Gather at ground.
Culture below.

Public ground / library above

Puthishala / Longitudinal section A-A / NTS

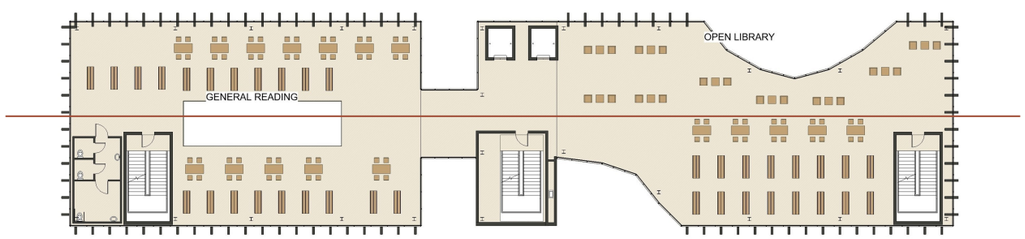

A-A / CUT LOCATION

- **READING / FOUR LEVELS**
- **PLAZA / PUBLIC GROUND**
- **FOYER / BELOW GROUND**

Programme in section

Puthishala / Sectional perspective / NTS

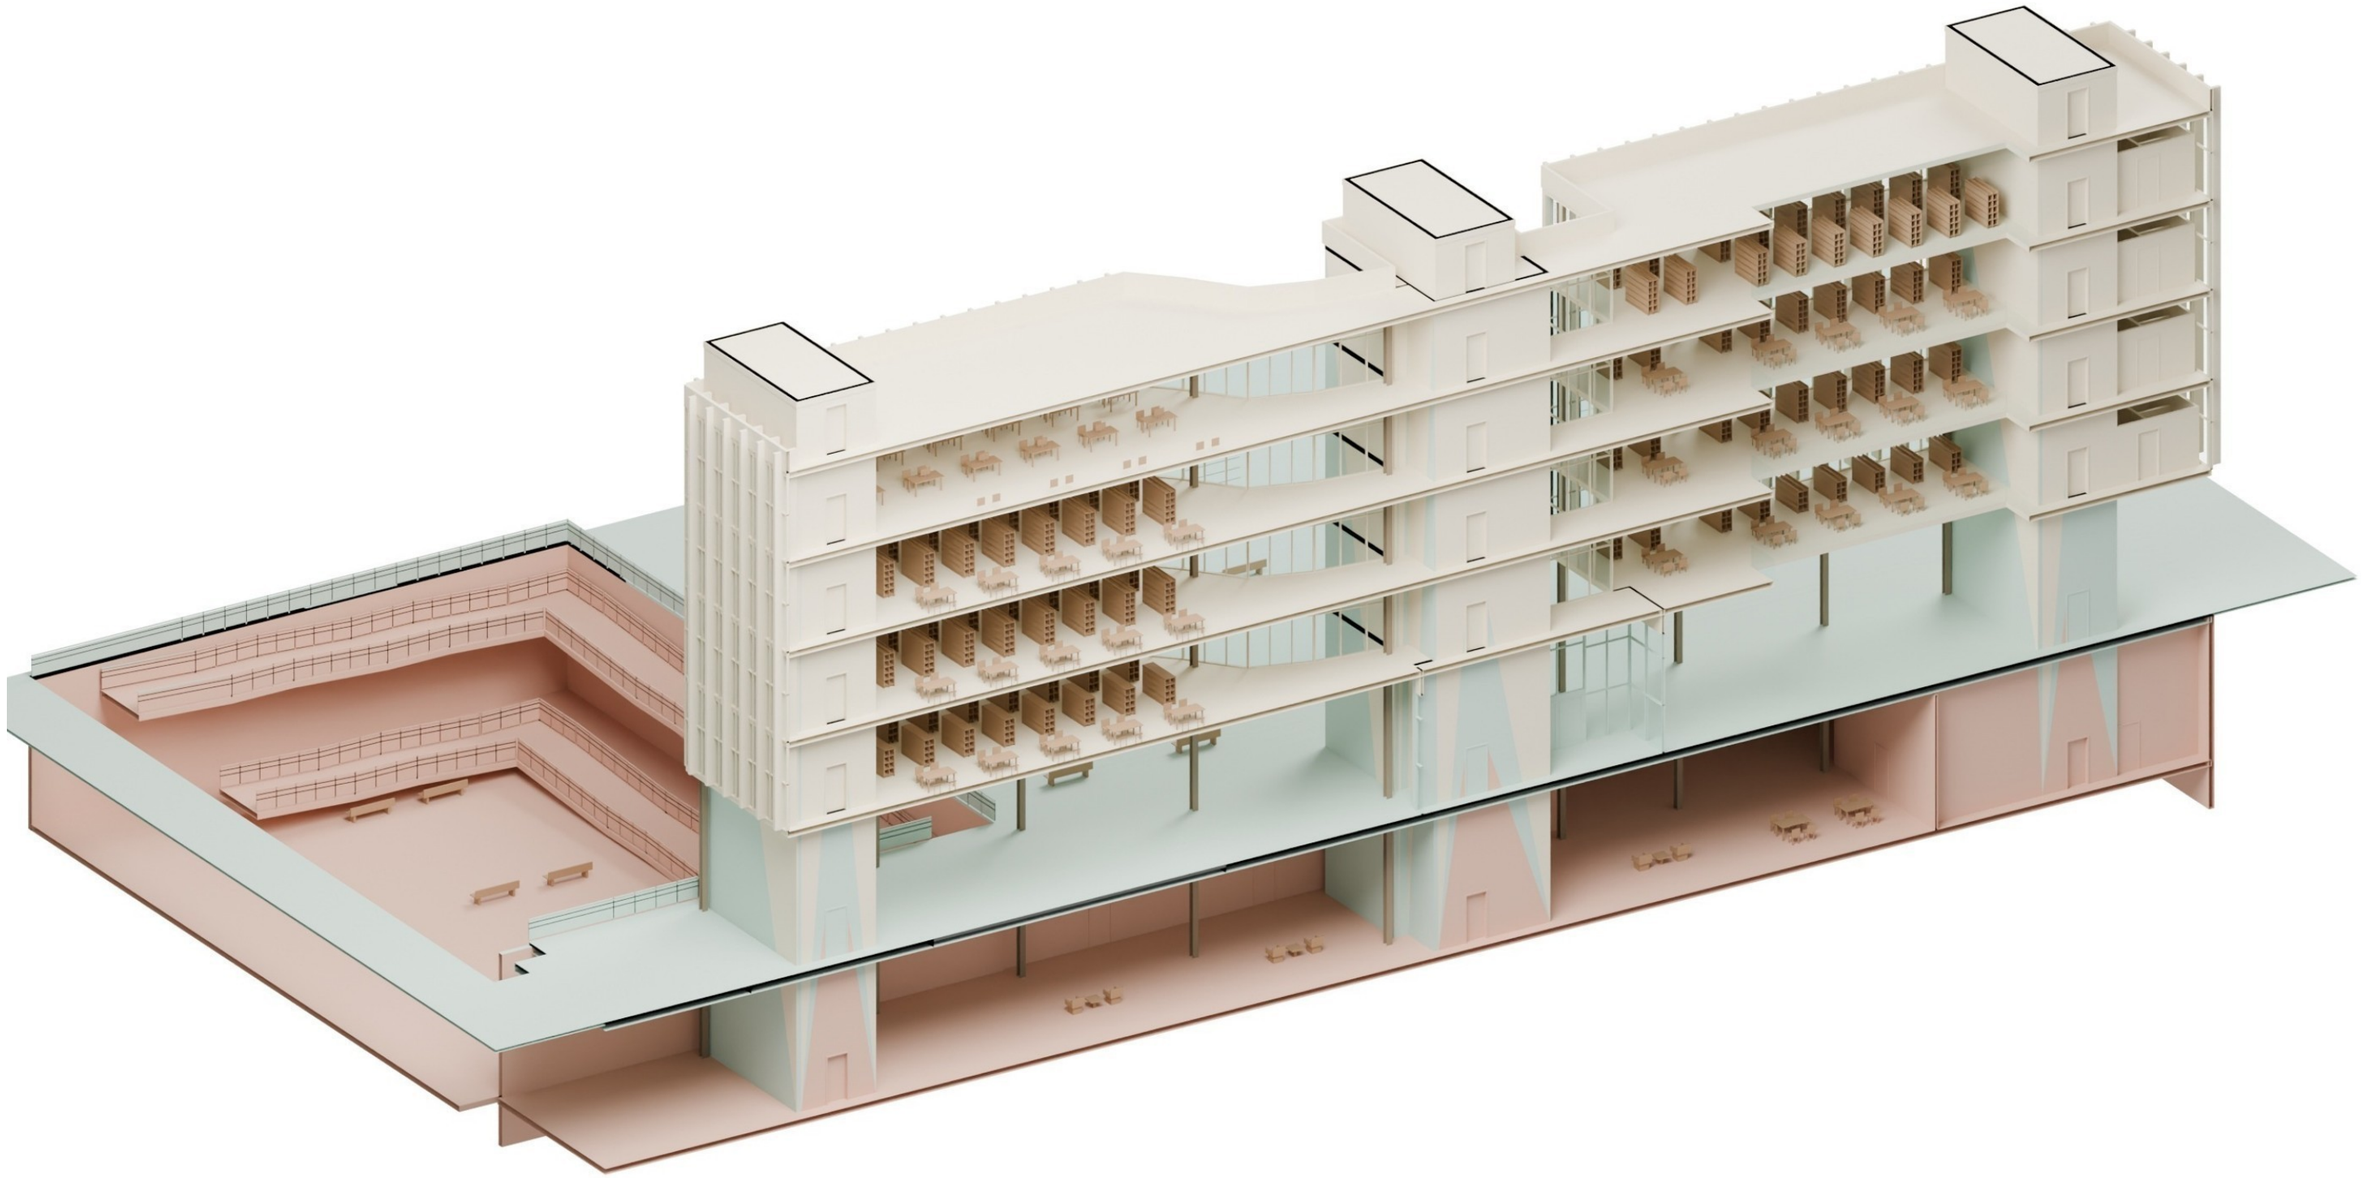

● 01 / READING

● 02 / PUBLIC GROUND

● 03 / CULTURE

Bhashantek Housing

Collective housing / Mirpur 14, Dhaka / Group academic project

SHARED COURTS

PEDESTRIAN CLUSTERS

PUBLIC WATER EDGE

Shared ground

Bhashantek / Courts, landscape & pedestrian routes

01 / MASTER PLAN

02 / SHARED LAWN

03 / SHADED ROUTE

04 / COMMON SPACE

From block to dwelling

Bhashantek / Original CAD / NTS

TYPE A / FLOORS 2 & 4

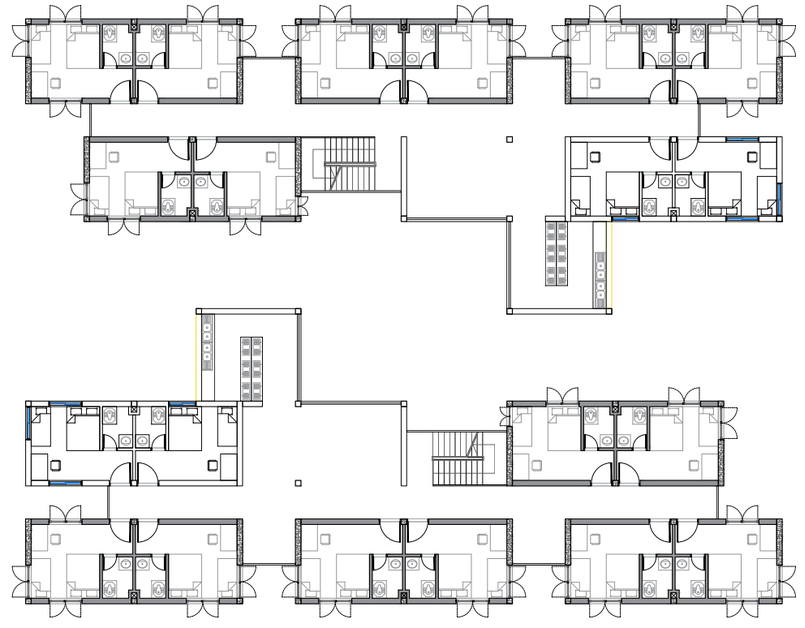

TYPE B / GROUND, 2 & 4

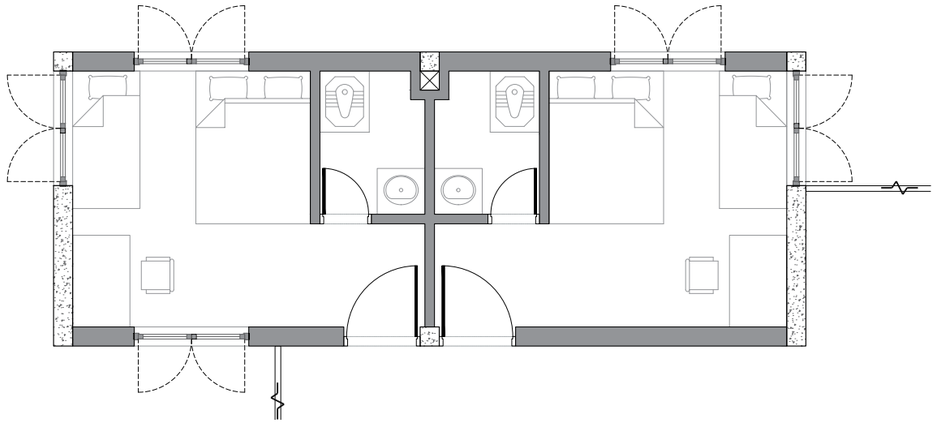

PAIRED DWELLING MODULE

Dwelling & shared access

Bhashantek / Section A-A & sectional perspective / NTS

01 / SECTION A-A

02 / SECTIONAL PERSPECTIVE

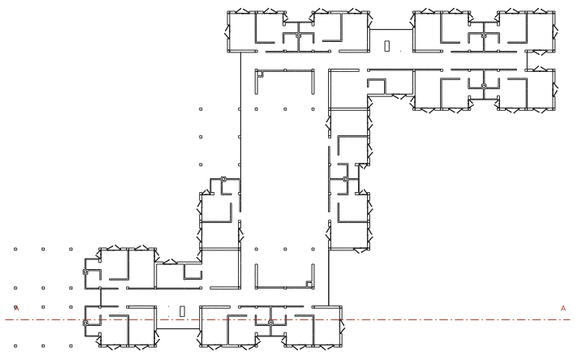

03 / CUT LOCATION

Sylhet Divisional Museum

Kumargaon, Sylhet / Individual academic design

DESIGN VISUALIZATION

The past above. The present at ground.

A descent through time

Museum / Atrium, ramp & exhibition galleries

DAYLIGHT / BOWL CANOPY

TOP LOBBY +24.384

GALLERY +18.288

GALLERY +12.192

GALLERY +7.620

RELIC COURT 0.000

6.25 turns / 2.30 m ramp / Sloping sectors approx. 1:20.5-1:22.5

The courtyard of the present

Museum / Kaalaa Pathor, water & shared seating

Arif Raihan / Academic design / Interior visualization / Relic proportions aligned to section; dimensions unmeasured

From past to present

Museum / Four gallery connections and a continuous chronological descent / NTS

01 / TOP LOBBY FLOORPLATE

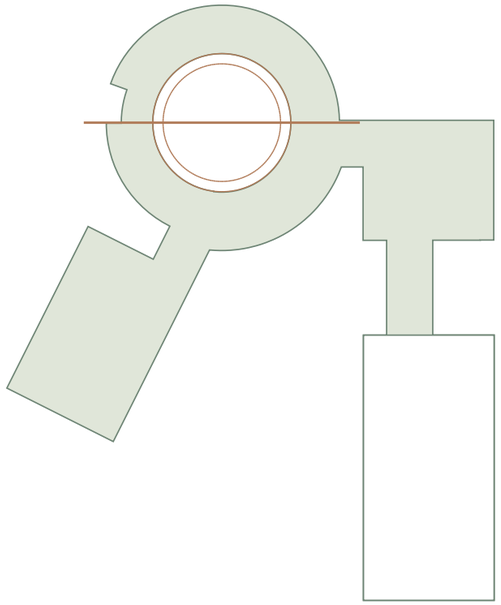

A-A

UP BY LIFT

One direct ascent to +24.384.

DOWN THROUGH HISTORY

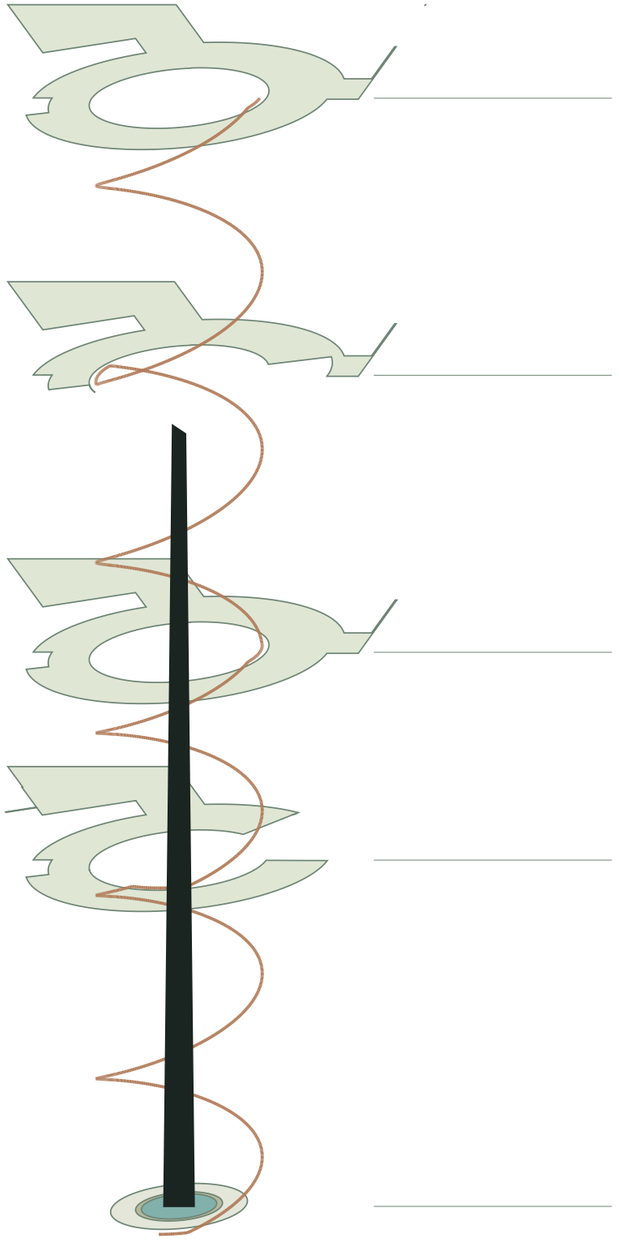

EXHIBITION WING + ATRIUM / 6.25 TURNS / 2.30 m RADIAL WIDTH

Light & rain

Museum / Architectural detail studies / NTS

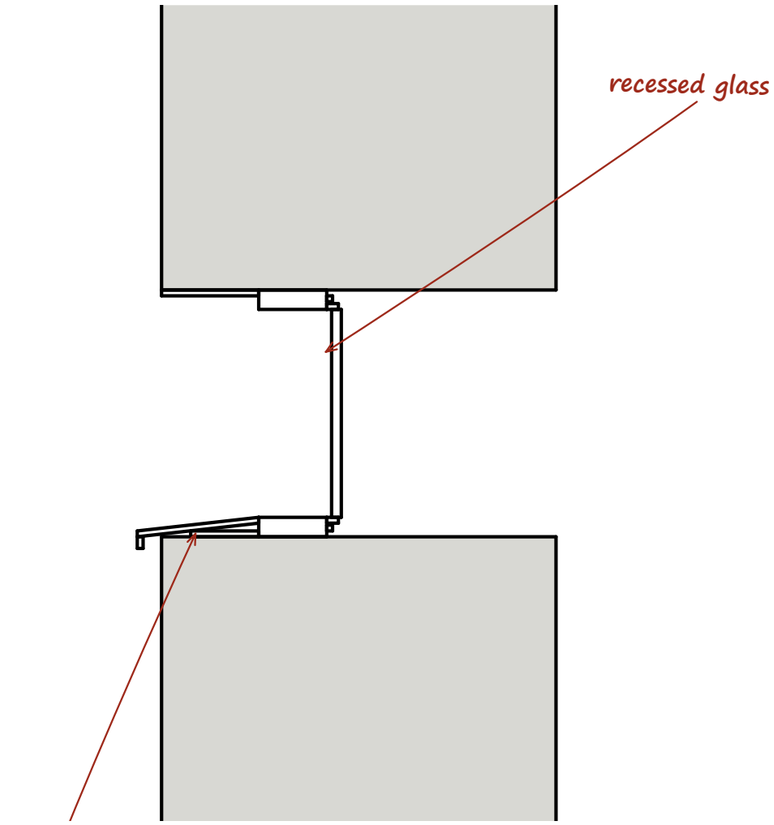

01 / RECESSED LIGHT SLOT

RECOVERED GLAZED BOWL
Concave source profile retained

PERIMETER WEATHER SKIRT
New closure to ring-roof curb

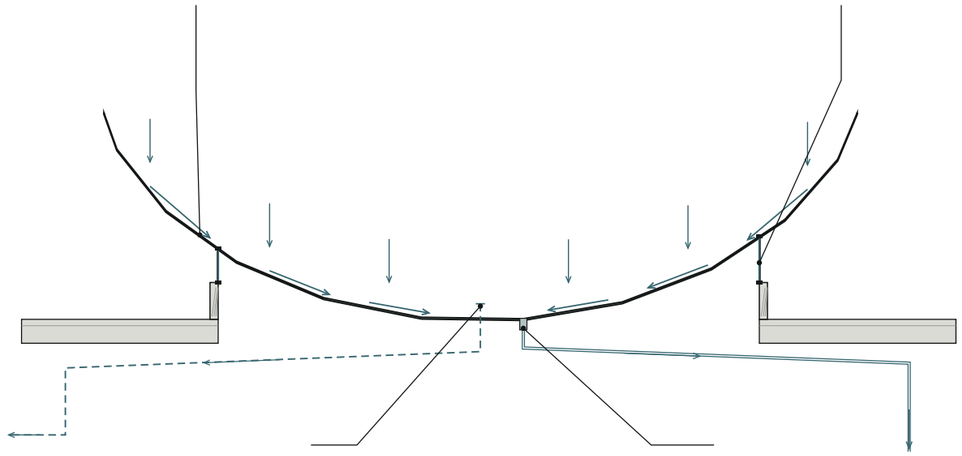

INDEPENDENT OVERFLOW
Raised intake / visible discharge

LOW-POINT COLLECTION
Closed primary drain

SECTION NTS / VERTICAL EXAGGERATION x4 / DRAINAGE STUDY
Solid blue: primary drain / Dashed blue: independent overflow

02 / BOWL ROOF & RAINWATER

Enclosure & movement

Museum / Facade & bridge studies / NTS

VISUAL STUDIES + DETAILS

COURTYARD

NORTH ENCLOSURE

ENCLOSED BRIDGE

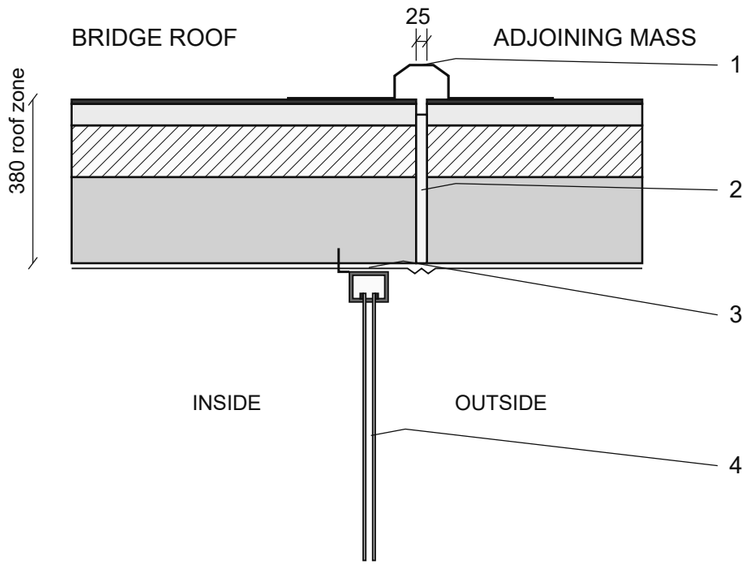

Nominal dimensions in mm / NTS

01 / Flexible roof cover

02 / Independent linings

03 / Slotted frame restraint

04 / Sealed glazing pocket

Ramp to gallery

Museum / Guard, arrival & exhibition route / NTS

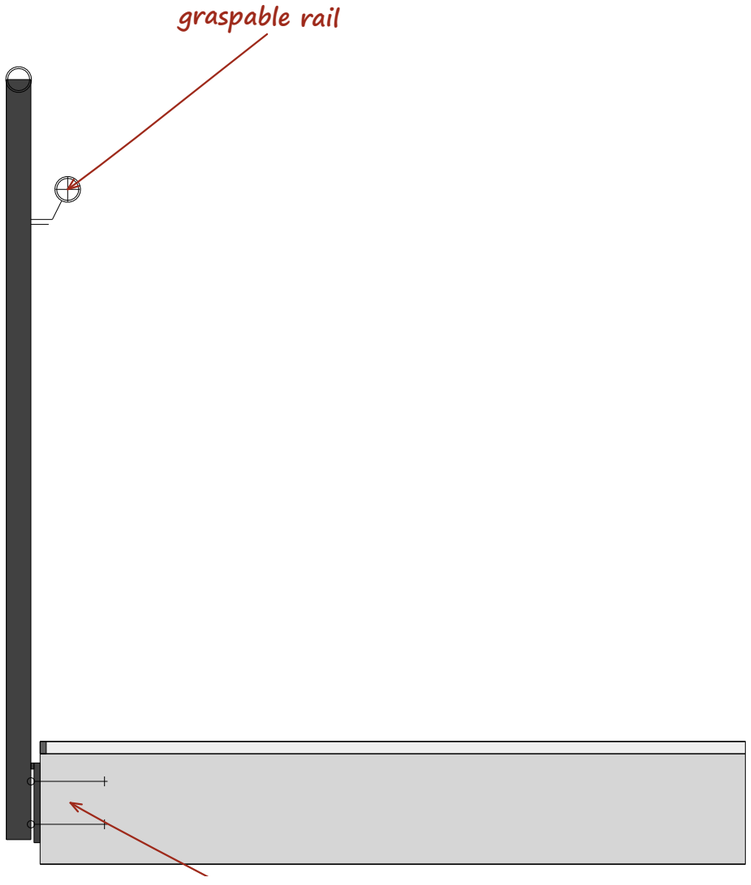

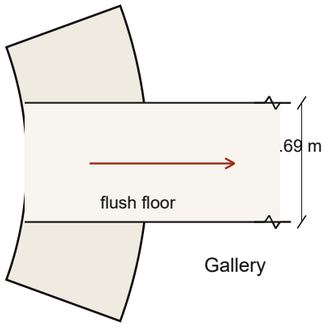

Graspable rail

Side-fixed guard

Flush gallery arrival

Arif Raihan

Dublin, Ireland

+353 89 208 0513

arif.raihan.bracuarch@gmail.com

linkedin.com/in/meister-arifraihan

PROFESSIONAL

Suvastu / Muskan Tower & Anandolok

Domus Architects / Shanta Forum HQ

Photography / City Syntax & project archives

ACADEMIC

BRAC University

Housing / Arif Raihan, Fariha Rahman & Monisha Sams

Puthishala & Museum / Arif Raihan

Original drawings and labelled development studies / Portfolio review / NTS